Руст. = 45,05 кВт
Ррасч. = 37,8 кВт
Iр = 67,6 А
Кс = 0,84
cos φ = 0,85

ВВГнг(А)-LS 5х25
к ВРУ-4

РП1

1QS
AR-SWN
3P 100A

L1,L2,L3
~400В

N

PE

Данные питающей сети																
Аппарат ввода Тип Номинальный ток, А Ток расцепителя, А																
Аппарат отходящей линии Тип, Номинальный ток, А Ток расцепителя, А	QF1.1 ВА47-60М С 63А	QF1.2 ВА47-60М С 6А	QF1.3 ВА47-60М С 6А	QF1.4 ВА47-60М С 20А	QF1.5 ВА47-60М С 20А	QF1.6 ВА47-60М С 6А	QF1.7 ВА47-60М С 20А	QF1.8 ВА47-60М С 6А	QF1.9 ВА47-60М С 10А	QF1.10 ВА47-60М С 10А	QF1.11 ВА47-60М С 25А	QF1.12 ВА47-60М С 3А	QF1.13 ВА47-60М С 3А	QF1.14 ВА47-60М С 20А	QF1.15 ВА47-60М С 16А	
Пусковой аппарат Тип, Номинальный ток, А Уставка, А Н.э. теплового реле, А	UZ1 22кВт	UZ2 0,75кВт	UZ3 0,75кВт	КМ1.1 КМИ-22510 25А	КМ1.2 КМИ-22510 25А	КМ1.3 КМИ-10910 АС 9А										
Марка, сечение проводника, длина, способ прокладки	ВВГнг(А)-LS 4х10	ВВГнг(А)-LS 4х1,5	ВВГнг(А)-LS 4х1,5	ВВГнг(А)-LS 4х1,5	ВВГнг(А)-LS 4х1,5	ВВГнг(А)-LS 4х1,5	ВВГнг(А)-LS 4х1,5	ВВГнг(А)-LS 4х1,5	ВВГнг(А)-LS 3х1,5	ВВГнг(А)-LS 3х1,5	ВВГнг(А)-LS 3х2,5	ВВГнг(А)-LS 3х1,5	ВВГнг(А)-LS 3х1,5			
Электроприемник: Наименование потребителя	РМ2.1	РМ3.1	РМ3.3	РМ1.1	РМ1.2	РМ3.5	Г1	Г4	ШУК1	ШУК2	ШЛСУ	В1.1, В1.2	ЦУ1			
Установленная мощность, кВт	22,0	0,37	0,37	5,6	5,6	1,1	5,6	0,85	0,3	0,3	2,5	0,06	0,4			
Расчетный ток, А	40,0	0,94	0,94	9,3	9,3	1,9	10,6	1,6	1,3	1,3	10,8	0,26	1,7			
Кс	0,5	0,5	0,5	1	1	0,5	1	1	1	1	1	1	1			
Фаза сети									L1	L1	L2	L3	L3			
cos φ	0,9	0,8	0,8	0,9	0,9	0,8	0,8	0,8	0,95	0,95	0,95	0,8	0,8			
Наименование помещения / установки	Циркуляционный насос N1 Т2.1	Циркуляционный насос N1 Т4	Циркуляционный насос N1 Т2.2	Котловой насос N1	Котловой насос N2	Подпиточный насос N1. Ввод ХВС	Газо-дизельная горелка N1	Газо-дизельная горелка N4	Шкаф управления котлом N1	Шкаф управления котлом N2	Шкаф управления автоматизирован. тепловым пунктом	Вентиляторы системы охлаждения	Цепи управления	Резерв	Резерв	

Взам. инв. №


Подп. и дата

Инв. № подл.


							3Н00-000015.26-ЭОМ
							Канализационные очистные сооружения в г. Тарко-Сале, в том числе затраты на проектно-изыскательские работы
Изм.	Кол.уч.	Лист	N док.	Подп.	Дата		
Разработал		Потанин			09.26	Модульная котельная установка Нео-Терм МКБИ/Г-Ж.6,2.В.1МК-0174	Стадия: Р; Лист: 1; Листов: 10
Проверил		Устюжанин			09.26		
Н. контроль		Ярославцева			09.26	Вводно-распределительное устройство. Схема электрическая однолинейная. Распределительная панель N1	НЕО ТЕРМ

Формат А2


Распределительная панель
Вид спереди с открытой дверью

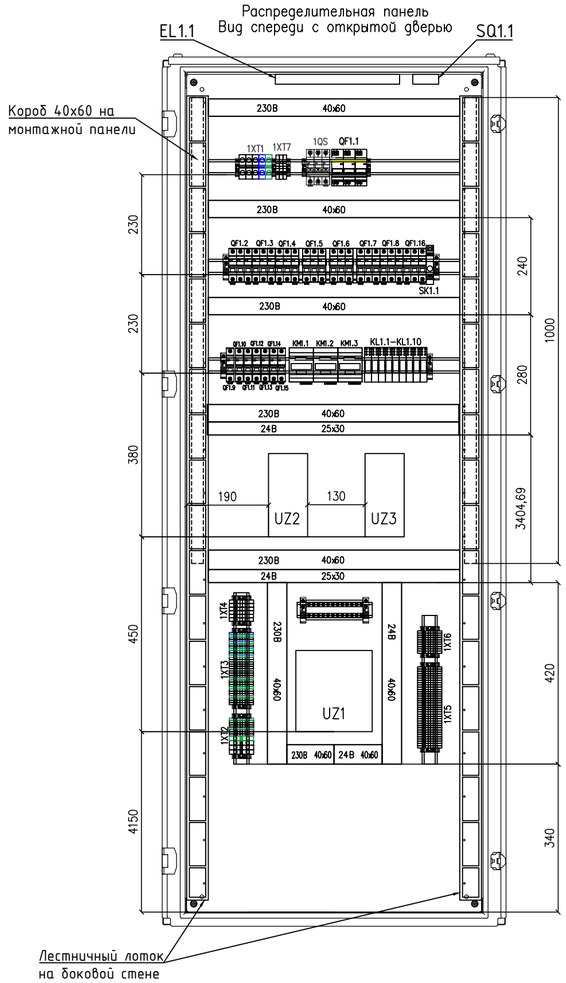


Распределительная панель
Вид спереди с закрытой дверью

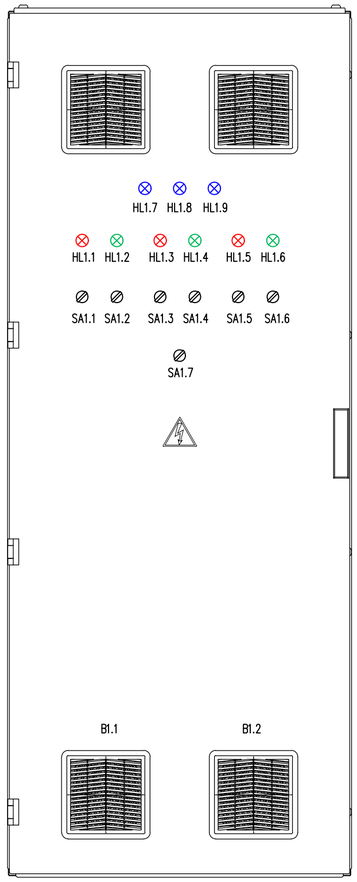


Вырезы под кабельные вводы
Вид сверху

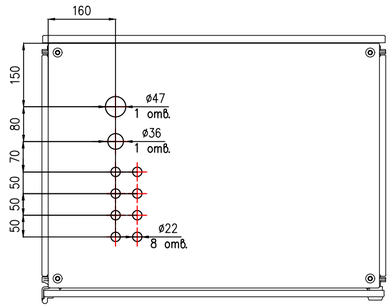

Вырезы под оборудование на двери
Вид спереди

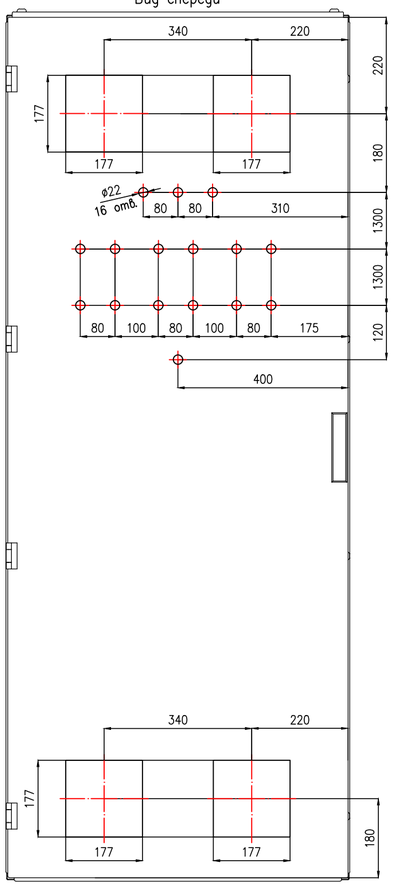

Вырезы под кабельные вводы
в полу. Вид снизу

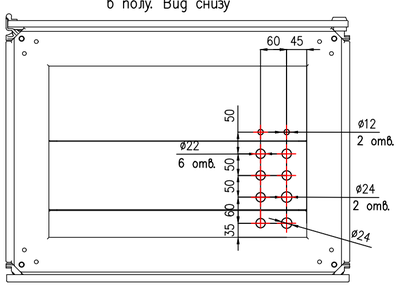

Поз.	Обозначение	Кол.	Примечание
		1	
1QS	Выключатель–разъединитель SWN 3P 100A (AR–SWN–3–100)	1	
QF1.1	Автоматический выключатель ВА47–60М С 63А 3Р (MVA31–3–063–С)	1	
QF1.2,QF1.3, QF1.6,QF1.8,	Автоматический выключатель ВА47–60М 3Р С 6А (MVA31–3–006–С)	4	
	Аварийный контакт КСВ47–60М для ВА47–60М (MVA31D–AK–1)	1	
QF1.4,QF1.5, QF1.7,QF1.14	Автоматический выключатель ВА47–60М С 20А 3Р (MVA31–3–020–С)	4	
	Аварийный контакт КСВ47–60М для ВА47–60М (MVA31D–AK–1)	2	
QF1.9,QF1.10	Автоматический выключатель ВА47–60М 1Р С 10А (MVA31–1–010–С)	2	
QF1.11	Автоматический выключатель ВА47–60М 1Р С 25А (MVA31–1–025–С)	1	
QF1.12, QF1.13	Автоматический выключатель ВА47–60М 1Р С 3А (MVA31–3–003–С)	2	
QF1.15	Автоматический выключатель ВА47–60М 1Р С 16А (MVA31–1–016–С)	1	
KM1.1, KM1.2	Контактор КМИ–22510 25А 230В (KKM21–025–230–10)	2	
KM1.3	Контактор КМИ–10910 9А 230В (KKM11–009–230–10)	1	
SK1.1	Термостат модульный NO диапазон температур –10–80 градусов	1	
HL1.1,HL1.3 HL1.5	Лампа AD22DS LED матрица 22мм зеленый 230В (BLS10–ADDS–230–K06)	3	
HL1.2,HL1.4 HL1.6	Лампа AD22DS LED матрица 22мм красный 230В (BLS10–ADDS–230–K04)	3	
HL1.7...HL1.9	Лампа AD22DS LED матрица 22мм красный 230В (BLS10–ADDS–230–K04)	3	
SA1.1...SA1.6	Переключатель LAY5–BD25 2 положения I–0 стандарт ручка BSW60–BD–2–K02	6	
SA1.7	Переключатель LAY5–BD33 3 положения I–0–II стандарт ручка BSW60–BD–3–K02	1	
EL1.1	Светильник LA 6 Вт / LED (LA 6 LED)	1	
SQ1.1	Концевой выключатель SW 01	1	
KL1.1...KL1.10	Реле промежуточное серии RFT, 2ПК, 230VAC, 8А (RFT2CO730)	10	
	Колодка для реле RFT, SRU08–E, винтовой зажим (SRU08–E)	10	
1XT1	Клемма винтовая проходная, 35 мм², серая (MTU–35)	3	
	Клемма винтовая проходная, 35 мм², синяя (MTU–35BL)	1	
	Клемма винтовая проходная, 35 мм², "Земля" (MTU–35PE)	1	
1XT2	Клемма винтовая проходная, 10 мм², серая (MTU–10)	3	
	Клемма винтовая проходная, 10 мм², "Земля" (MTU–10PE)	1	
	Клемма винтовая проходная, 2.5 мм², серая (MTU–2.5)	6	
	Клемма винтовая проходная, 2.5 мм², "Земля" (MTU–2.5PE)	2	
1XT3	Клемма винтовая проходная, 2.5 мм², серая (MTU–2.5)	18	
	Клемма винтовая проходная, 2.5 мм², синяя (MTU–2.5BL)	3	
	Клемма винтовая проходная, 2.5 мм², "Земля" (MTU–2.5PE)	9	
1XT4	Клемма винтовая с держателем предохранителя, 4 мм2, серая	6	
1XT5	Клемма винтовая проходная, 2.5 мм², серая (MTU–2.5)	36	
1XT6	Клемма винтовая проходная, 2.5 мм², серая (MTU–2.5)	10	
1XT7	Клемма винтовая с держателем предохранителя, 4 мм2, серая	3	
B1.1, B1.2	Вентилятор фильтрующий 272м3/ч, 230В, 31Вт, IP54 (FA 13.230 FD)	2	

							3Н00–000015.26–ЭОМ
							Канализационные очистные сооружения в г. Тарко–Сале, в том числе затраты на проектно–изыскательские работы
Изм.	Кол.уч.	Лист	N док.	Подп.	Дата		
Разработал		Потанин			09.26	Модульная котельная установка Нео–Терм МКБИ/Г–Ж.6,2.В.1МК–0174	Стадия: Р; Лист: 2; Листов: 10
Проверил		Устюжанин			09.26		
Н. контроль		Ярославцева			09.26	Вводно–распределительное устройство ВРУ. Компоновочный чертеж. Распределительная панель N1	НЕО ТЕРМ

Взам. инв. №
Подп. и дата
Инв. № подл.

Формат А2

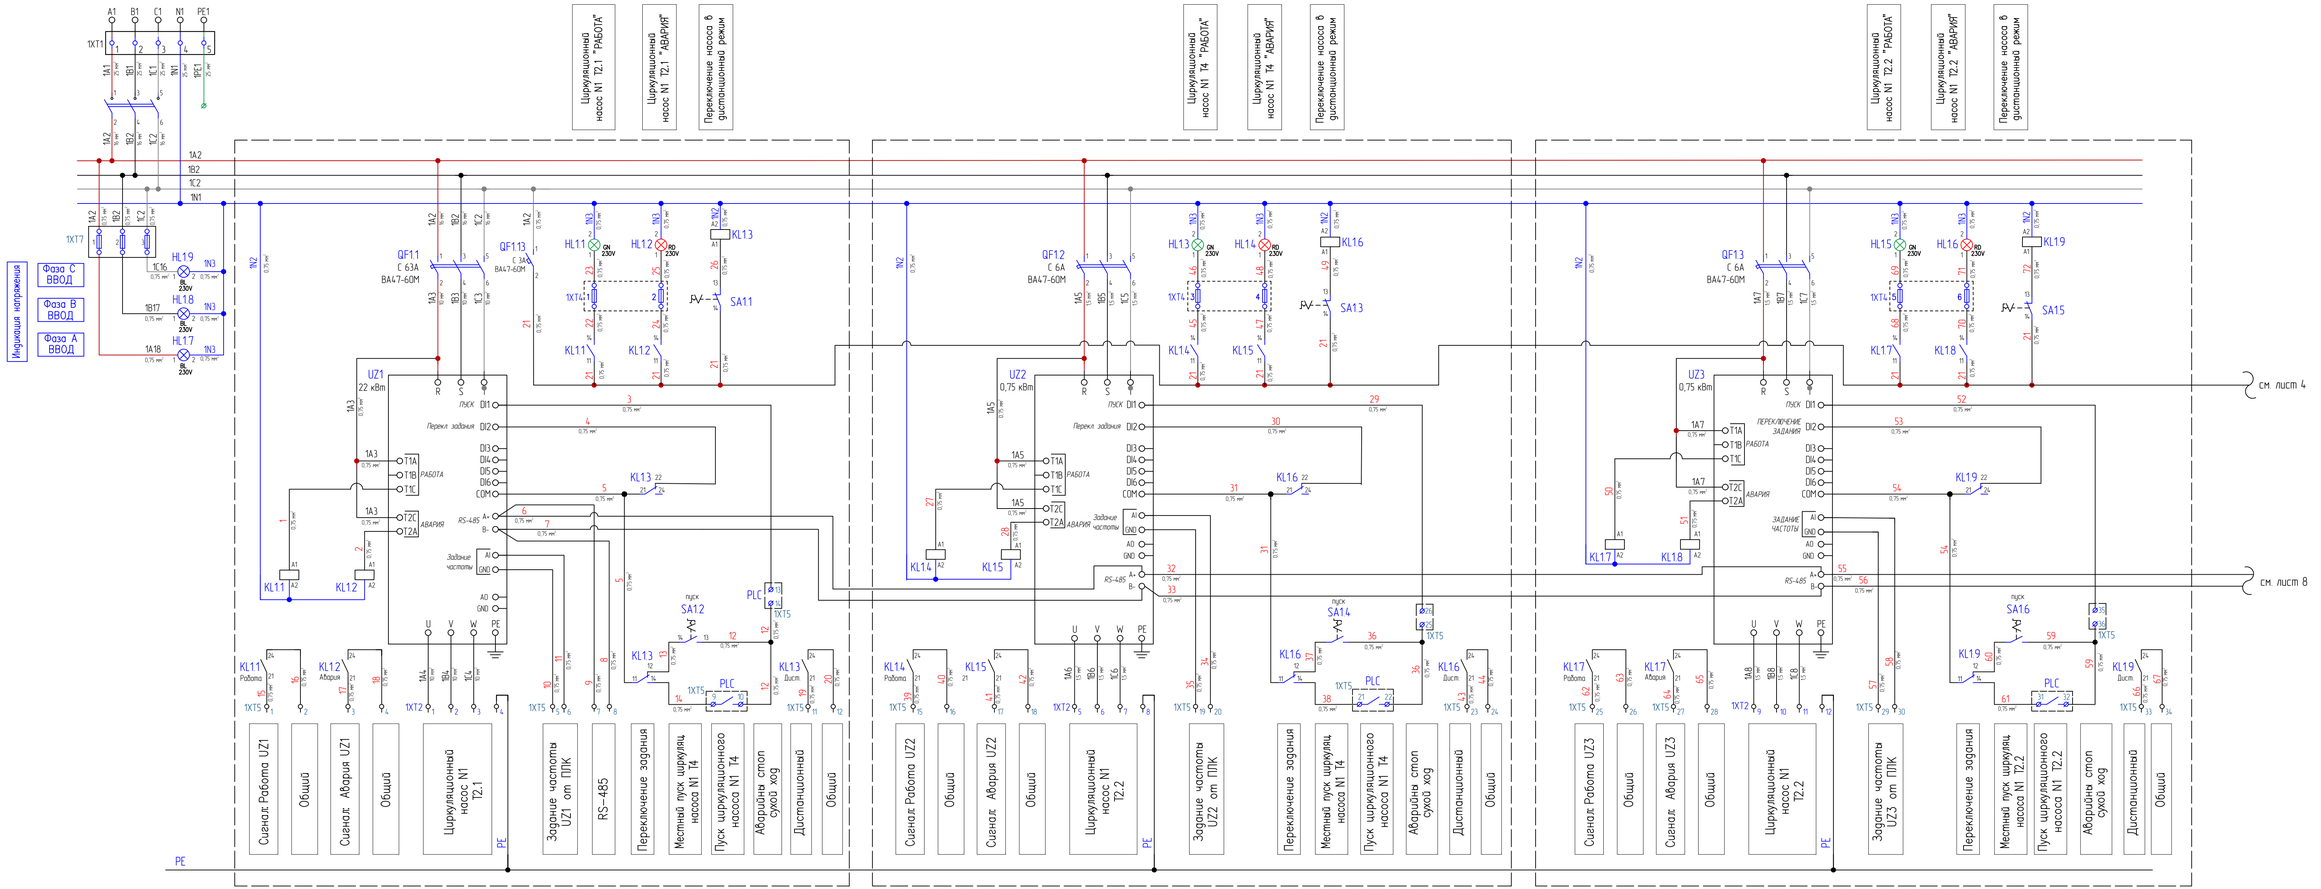


Диаграмма работы SA11		
Контакты	13–14	–
Положение		
1– Дист. режим	X	–
2– Местн. режим	–	–

Диаграмма работы SA12		
Контакты	–	13–14
Положение		
1– Стоп	–	–
2– Местн. пуск	–	X

Диаграмма работы SA13		
Контакты	13–14	–
Положение		
1– Дист. режим	X	–
2– Местн. режим	–	–

Диаграмма работы SA14		
Контакты	–	13–14
Положение		
1– Стоп	–	–
2– Местн. пуск	–	X

Диаграмма работы SA15		
Контакты	13–14	–
Положение		
1– Дист. режим	X	–
2– Местн. режим	–	–

Диаграмма работы SA16		
Контакты	–	13–14
Положение		
1– Стоп	–	–
2– Местн. пуск	–	X

Изм.	Кол.уч.	Лист	N док.	Подп.	Дата
Разработал		Потанин			09.26
Проверил		Устюжанин			09.26
Н. контроль		Ярославцева			09.26

ЗН00–000015.26–ЭОМ

Канализационные очистные сооружения в г. Тарко–Сале, в том числе затраты на проектно–изыскательские работы

Модульная котельная установка Нео–Терм МКБИ/Г–Ж6,2.В.1МК–0174

Стадия	Лист	Листов
Р	3	10

Схема электрическая принципиальная. Распределительная панель N1.

НЕО ТЕРМ

Формат А3х3

Взам. инв. №

Подп. и дата

Инв. № подл.

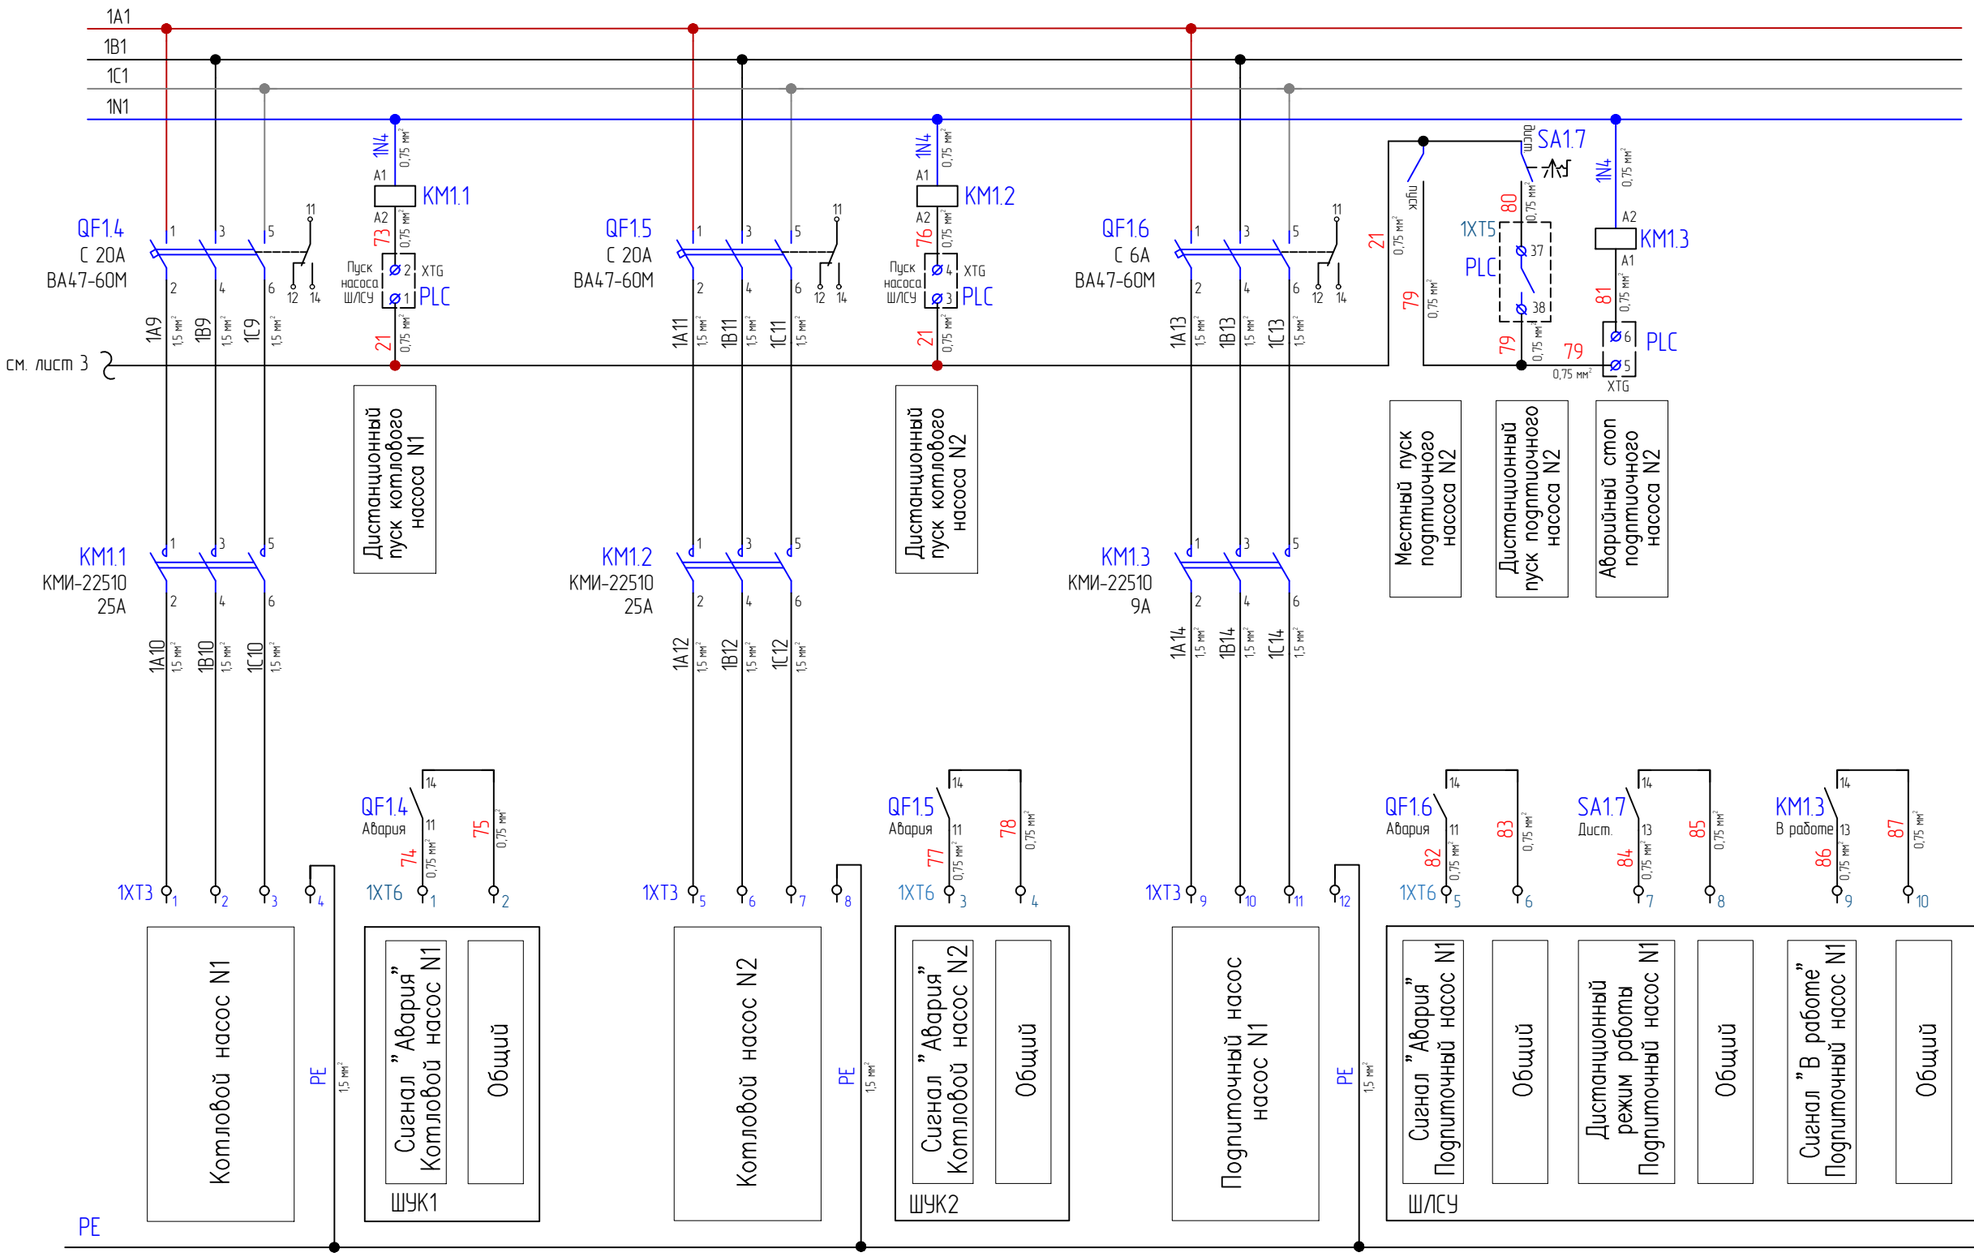


Диаграмма работы SA1.7

Контакты / Положение	13–14	23–24
1 – Дист. режим	X	–
0 – Стоп	–	–
2 – Мест. пуск	–	X

Изм.	Кол.уч.	Лист	N док.	Подп.	Дата
Разработал		Потанин			09.26
Проверил		Устюжанин			09.26
Н. контроль		Ярославцева			09.26

3Н00–000015.26–ЭОМ

Канализационные очистные сооружения в г. Тарко–Сале, в том числе затраты на проектно–изыскательские работы

Модульная котельная установка Нео–Терм МКБИ/Г–Ж.6,2.В.1МК–0174

Стадия	Лист	Листов
Р	4	10

Схема электрическая принципиальная. Распределительная панель N1.


НЕО ТЕРМ

Формат А3

Взам. инв. №

Подп. и дата

Инв. № подл.

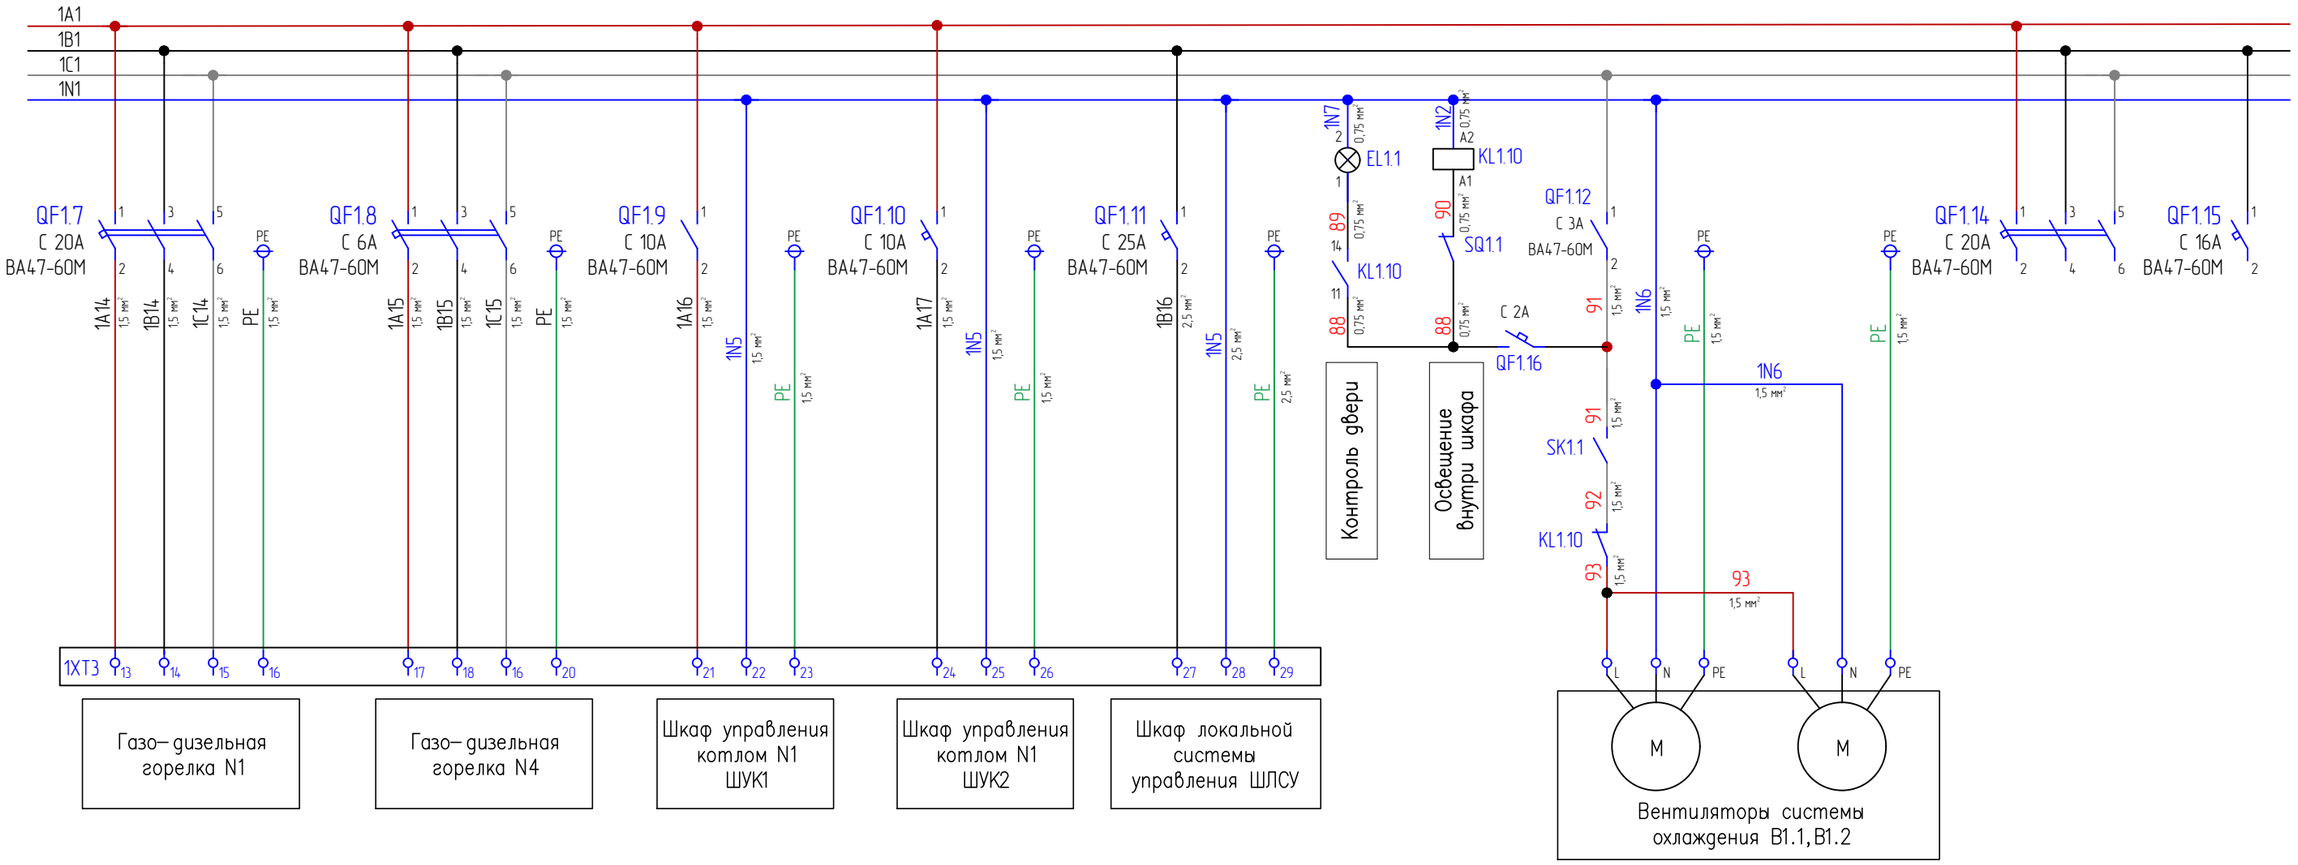

Изм.	Кол.уч.	Лист	N док.	Подп.	Дата
Разработал		Потанин			09.26
Проверил		Устюжанин			09.26
Н. контроль		Ярославцева			09.26

3Н00-000015.26-ЭОМ

Канализационные очистные сооружения в г. Тарко-Сале, в том числе затраты на проектно-изыскательские работы

Модульная котельная установка Нео-Терм МКБИ/Г-Ж.6,2.В.1МК-0174

Стадия	Лист	Листов
Р	5	10

Схема электрическая принципиальная. Распределительная панель N1.

НЕО ТЕРМ

Формат А3

Взам. инв. №

Подп. и дата

Инв. № подл.