
Принципиальная схема топливоснабжения

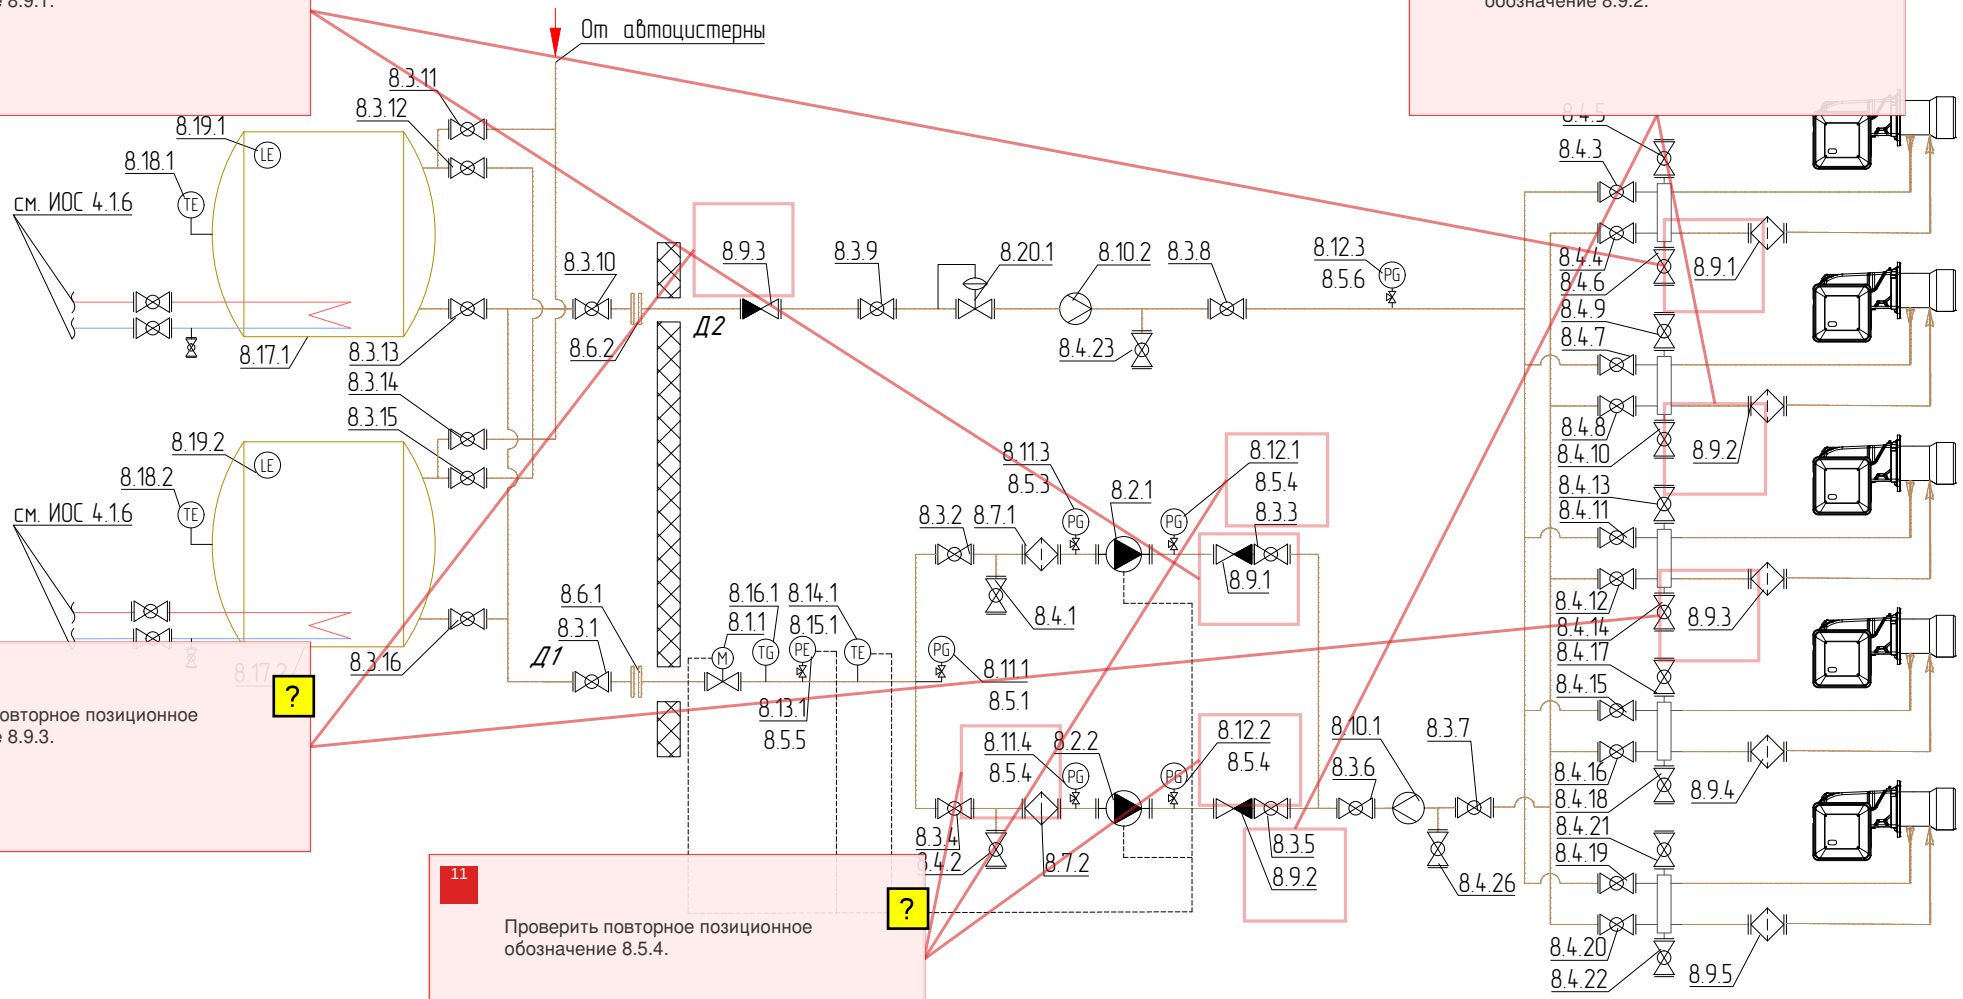

12 Проверить повторное позиционное обозначение 8.9.1.

13 Проверить повторное позиционное обозначение 8.9.2.

14 Проверить повторное позиционное обозначение 8.9.3.

11 Проверить повторное позиционное обозначение 8.5.4.

УСЛОВНЫЕ ОБОЗНАЧЕНИЯ

- регулятор давления
- трехходовой кран
- шаровый кран
- расходомер
- насос
- обратный клапан
- фильтр
- манометр
- термометр
- датчик давления
- датчик температуры

Изм.	Кол.уч.	Лист	N док.	Подп.	Дата
Разработал		Мазилюк			09.26
Проверил		Ахметов			09.26
Н.Контроль		Ярославцева			09.26
ГИП		Устюжанин			09.26

120/155-16-ИОС4.1.7-ГЧ

Блочно-модульная котельная со складом дизельного топлива на Объекте (шифр Объекта 120/155-16)

Тепломеханические решения зоны 6

Стадия	Лист	Листов
П	4	

Принципиальная схема топливоснабжения

ООО "Взлет-МСК"

Формат А4

Согласовано

Взам. инв. N

Подп. и дата

Инв. N подл.